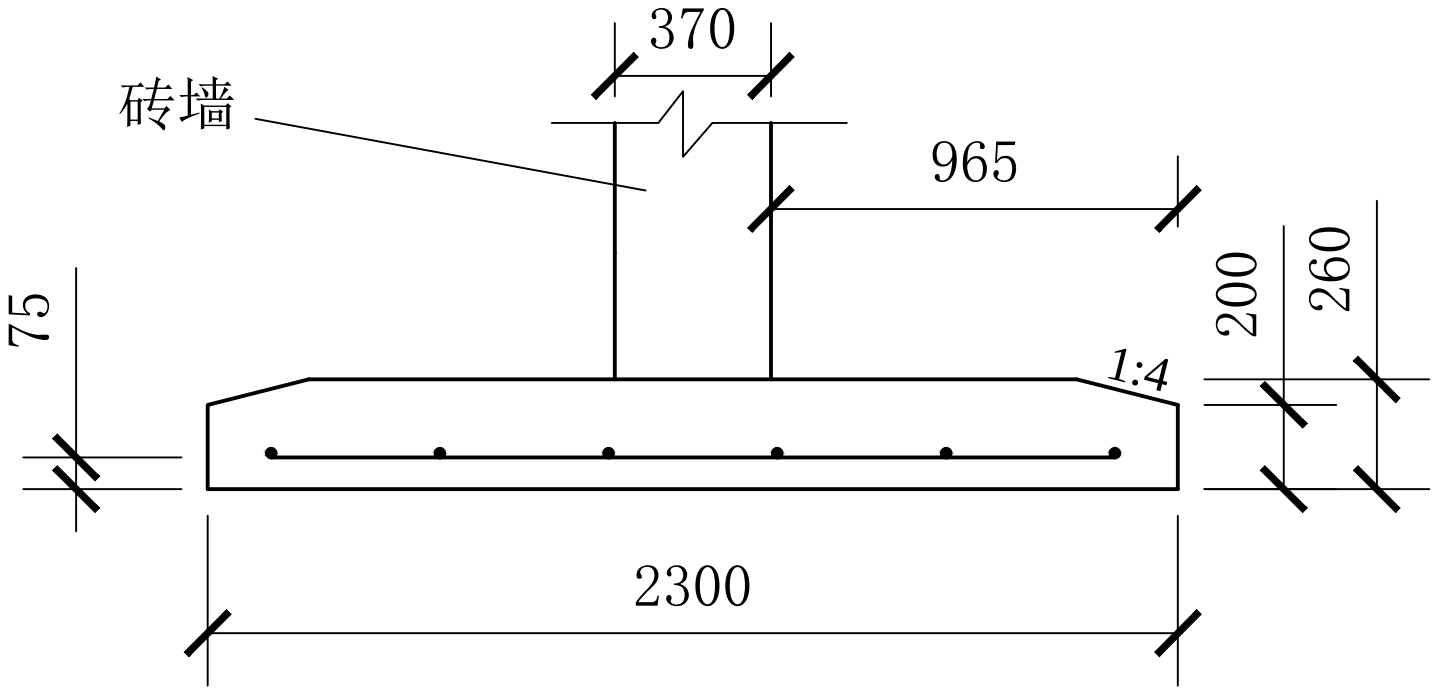
370
砖墙
965
75
200
260
1:4
2300